


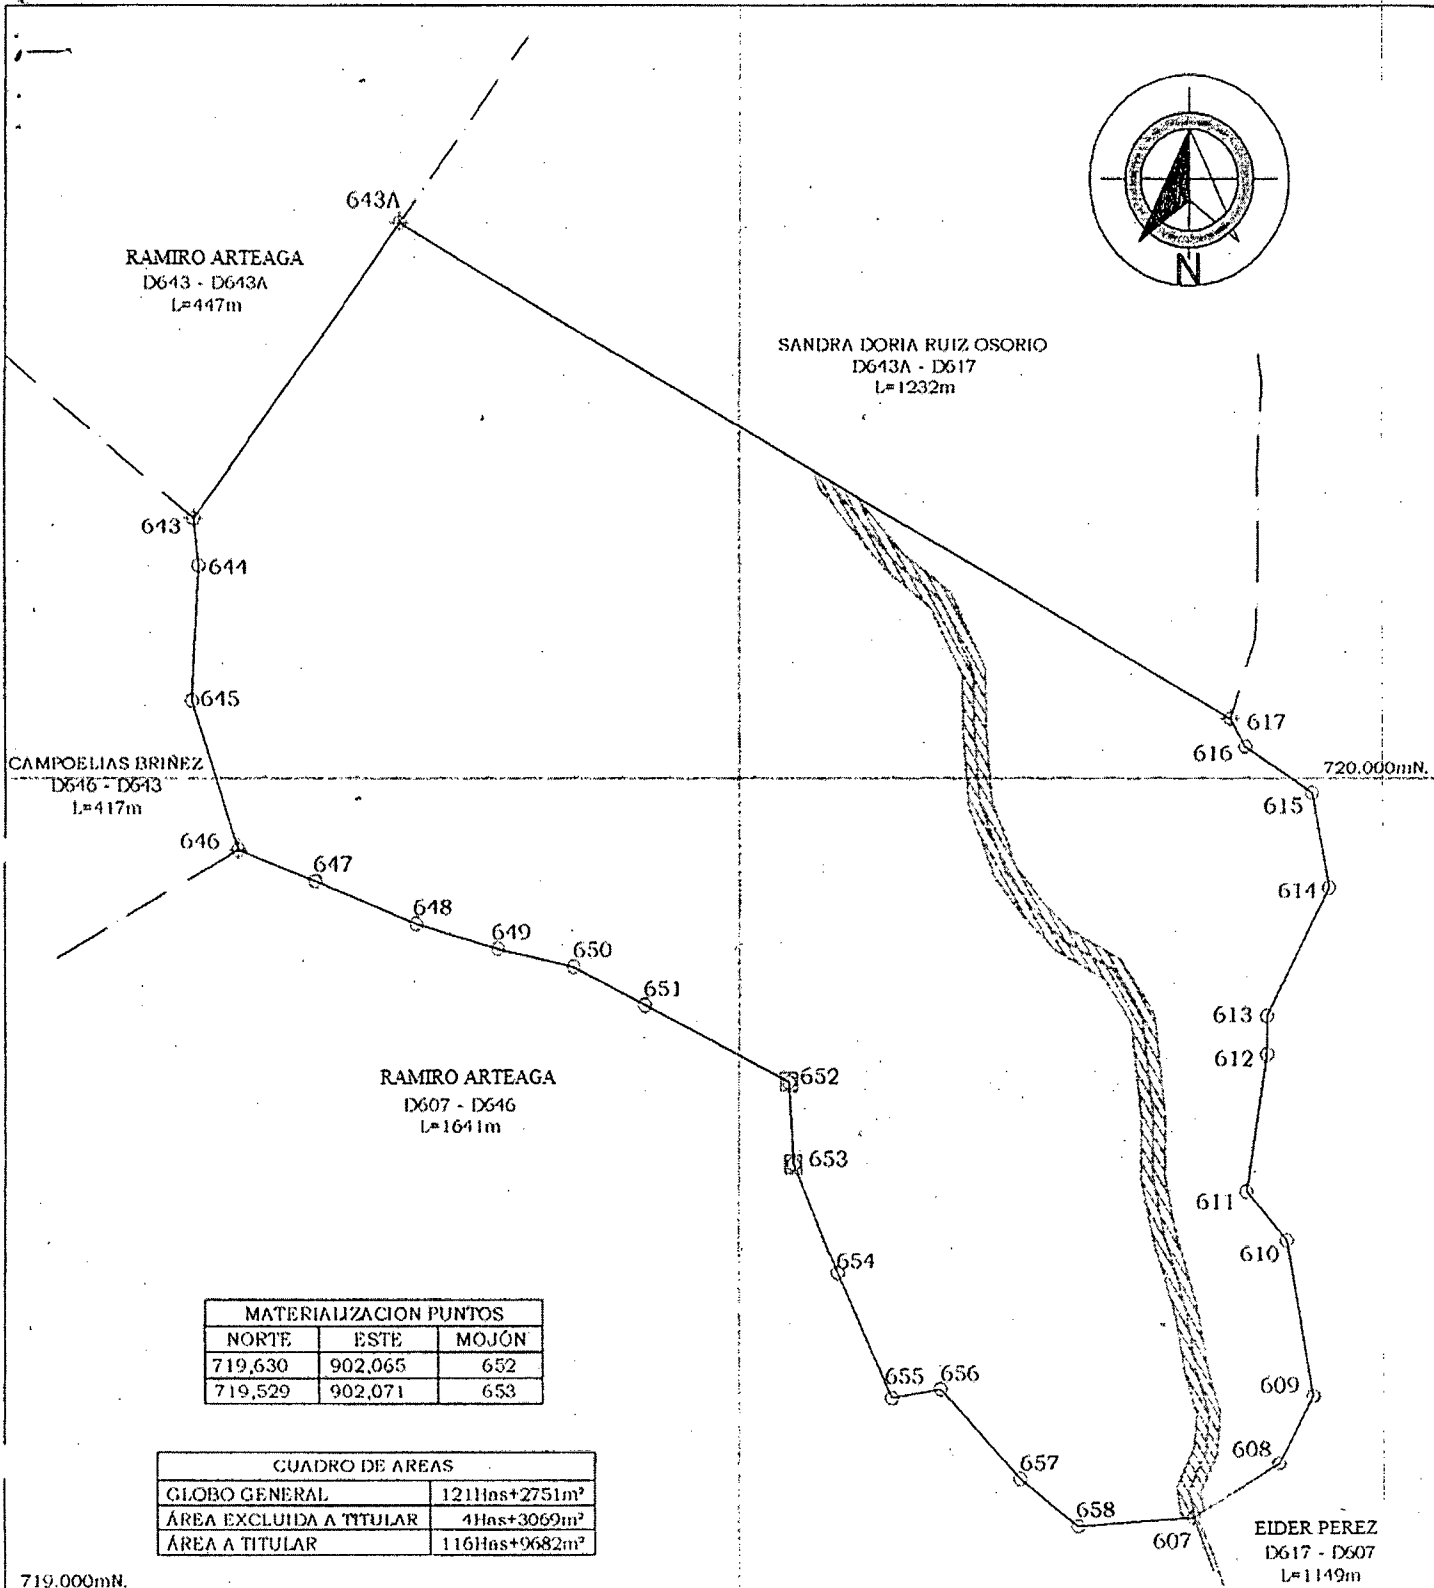

MATERIALIZACION PUNTOS		
NORTE	ESTE	MOJÓN
719,630	902,065	652
719,529	902,071	653

CUADRO DE AREAS	
GLOBO GENERAL	1211Has+2751m²
AREA EXCLUIDA A TITULAR	4Has+3069m²
AREA A TITULAR	116Has+9682m²

719.000mN.

CUADRO DE COORDENADAS Y COLINDANTES				
PUNTO	NORTE	ESTE	COLINDANTE	DISTANCIA
643A	720.682	901.561	SANDRA DORIA RUIZ OSORIO	1232m
617	720.075	902.633	EIDER PEREZ	1149m
607	719.095	902.587	RAMIRO ARTEAGA	1641m
646	719.913	901.355	CAMPOELIAS BRINEZ	417m
643	720.320	901.298	RAMIRO ARTEAGA	447m
643A	720.682	901.561	RAMIRO ARTEAGA	

Origen de las Coordenadas Planas:
BOGOTA_MAGNA SIRGAS
Latitud 04°35'46.3215"N. Longitud: 74°04'39.0285"W
Norte: 1000 000.0m Este: 1000 000.0m

CONVENCIONES	
Lindero del título	—
Rios	—
Quebradas	—
Lago - Laguna	—
Playon - Arenales	—
Colindancia	—
Radiación	—
Materializado	—
Camino - Sendero	—
Carretera	—
Via	—

ALTURA PROMEDIO = 443.00 m.s.n.m.

LEVANTO: LUIS FRANCISCO VALENCIA L.P. No 01-0840 C.P.N.T
CALCULO: LUIS FRANCISCO VALENCIA
DIBUJO: MAURICIO V / 311 499 7931
REVISO: _____
FECHA: MARZO 04 DE 2010
ESCALA: 1: 10.000

PREDIO: EL DIVISO II
VEREDA: ALTO RIECITO
MUNICIPIO: SAN VICENTE DEL CAGUAN
DEPARTAMENTO: CAQUETA
PROPIETARIO: MARGARITA REYES MURCIA
AREA A TITULAR 116Has+9682m²

OBRA No _____

ARCHIVO No 18-753001365