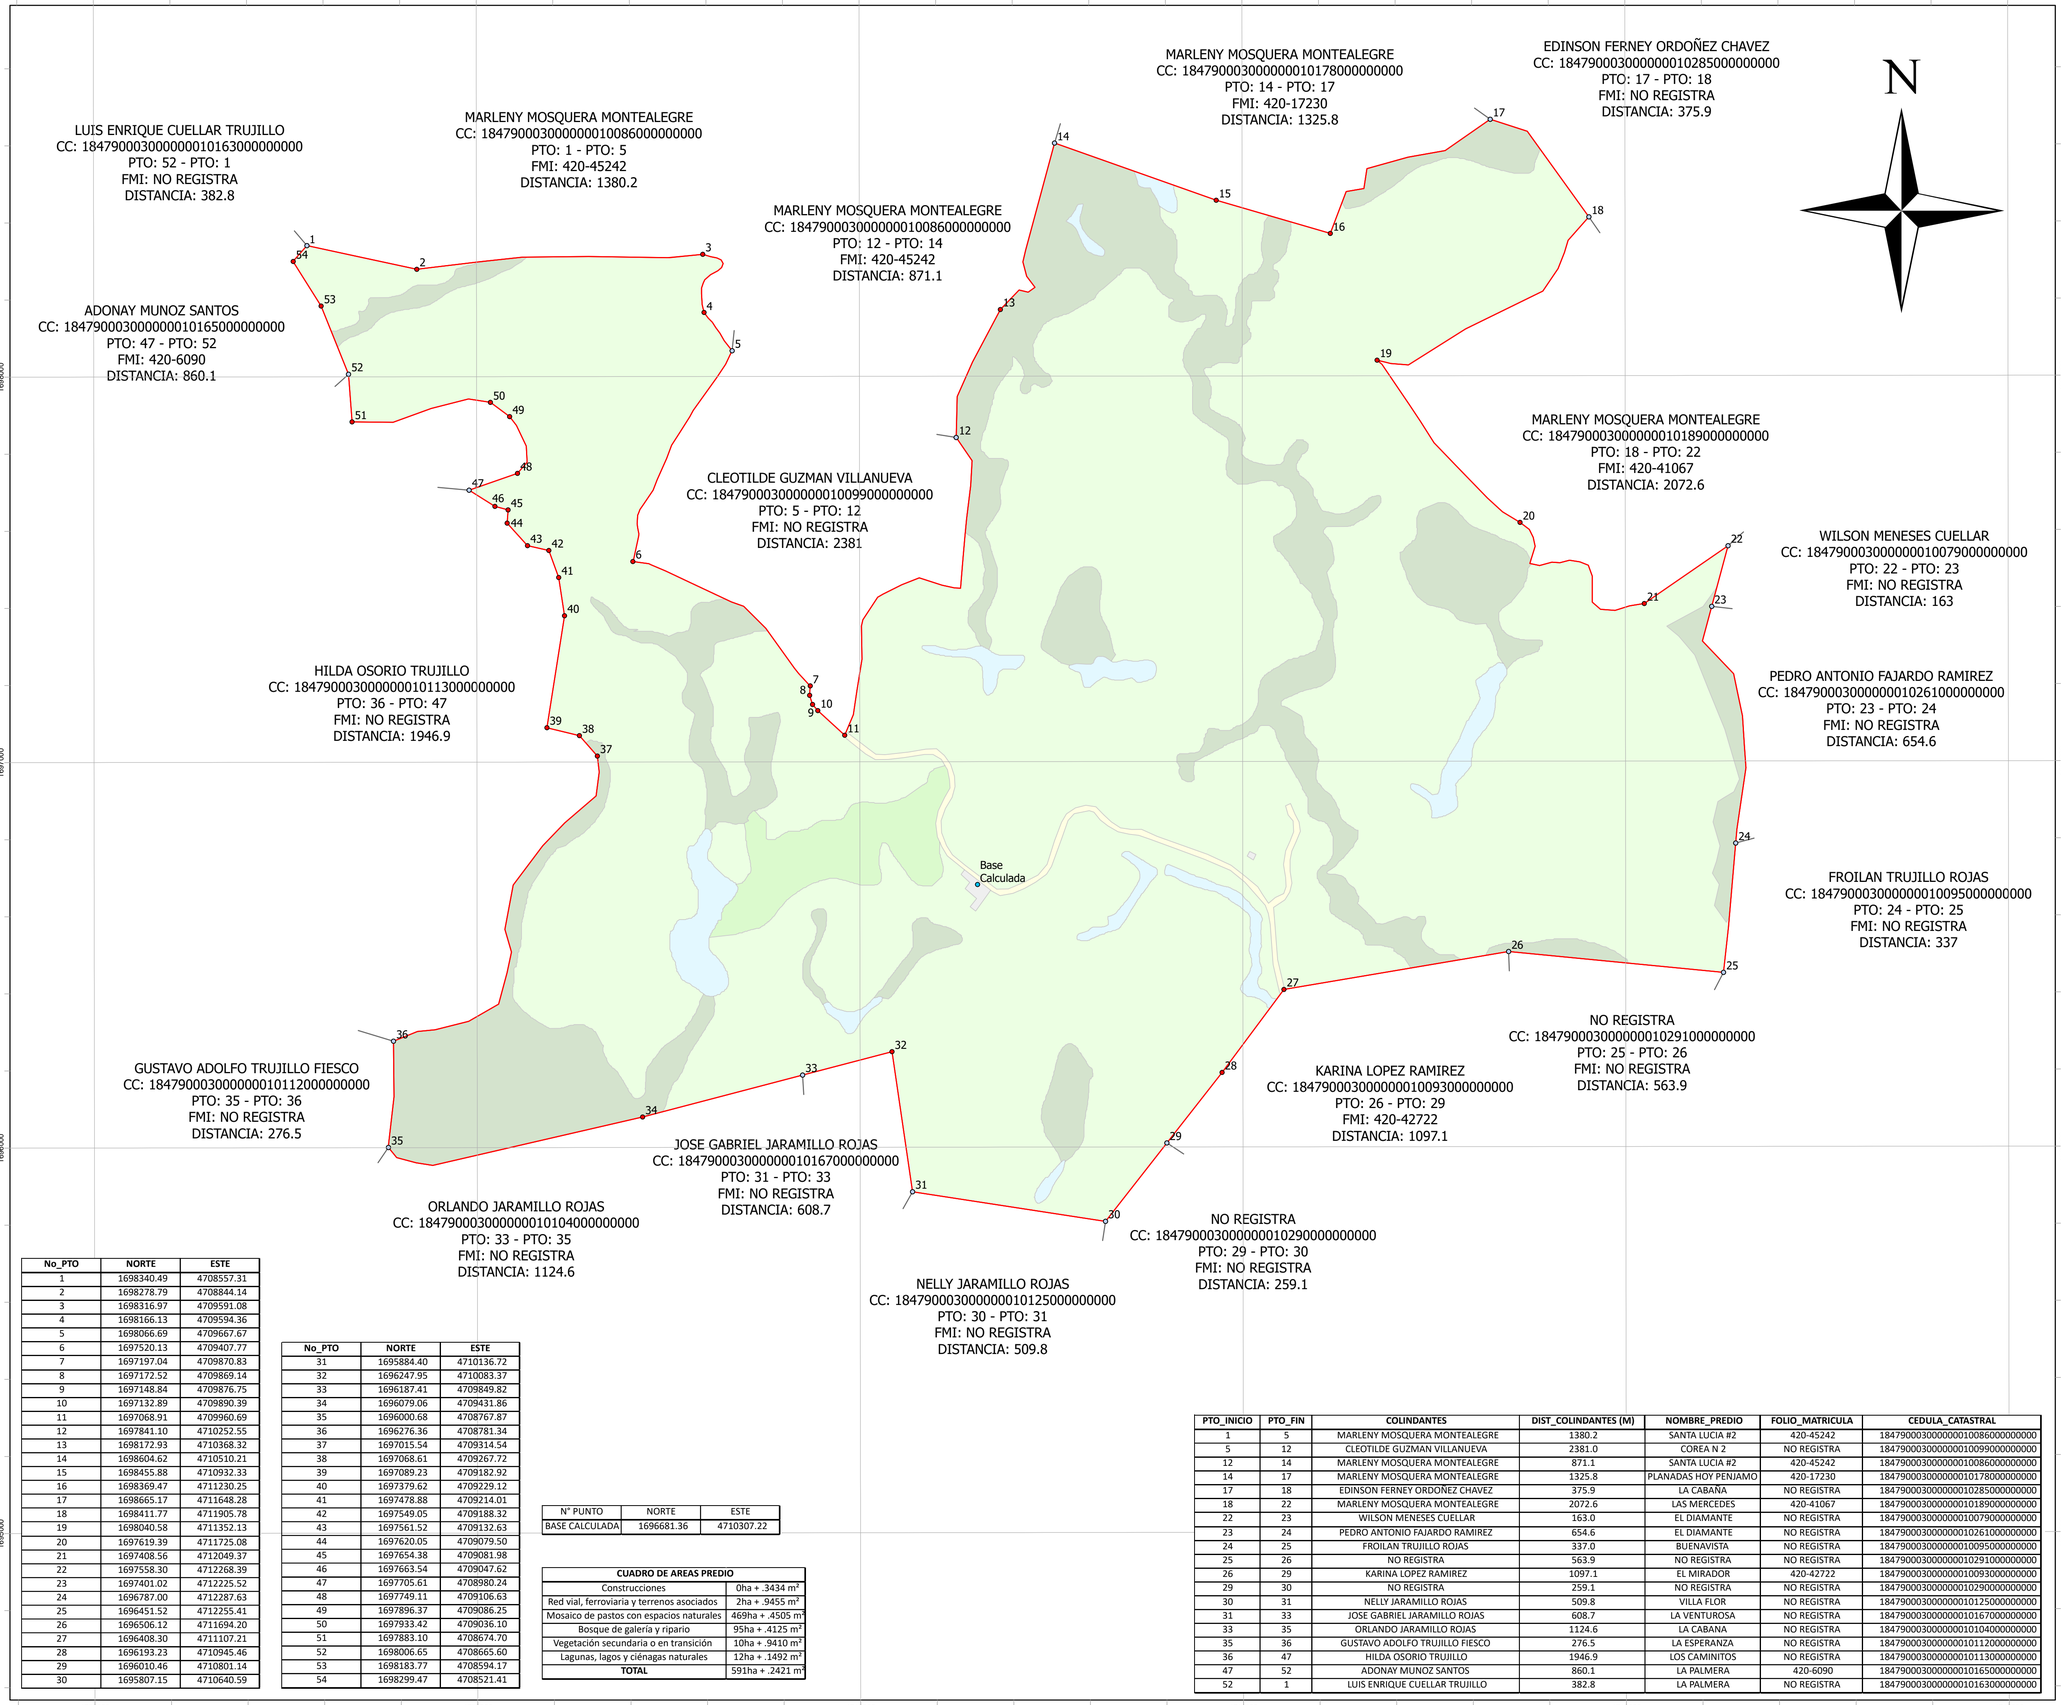

No_PTO	NORTE	ESTE
1	1698340.49	4708557.31
2	1698278.79	4708844.14
3	1698316.97	4709591.08
4	1698166.13	4709594.36
5	1698066.69	4709667.67
6	1697520.13	4709407.77
7	1697197.04	4709870.83
8	1697172.52	4709869.14
9	1697148.84	4709876.75
10	1697132.89	4709890.39
11	1697068.91	4709960.69
12	1697841.10	4710252.55
13	1698172.93	4710368.32
14	1698604.62	4710510.21
15	1698455.88	4710932.33
16	1698369.47	4711230.25
17	1698665.17	4711648.28
18	1698411.77	4711905.78
19	1698040.58	4711352.13
20	1697619.39	4711725.08
21	1697408.56	4712049.37
22	1697558.30	4712268.39
23	1697401.02	4712225.52
24	1696787.00	4712287.63
25	1696451.52	4712255.41
26	1696506.12	4711694.20
27	1696408.30	4711107.21
28	1696193.23	4710945.46
29	1696010.46	4710801.14
30	1695807.15	4710640.59

No_PTO	NORTE	ESTE
31	1695884.40	4710136.72
32	1696247.95	4710083.37
33	1696187.41	4709849.82
34	1696079.06	4709431.86
35	1696000.68	4708767.87
36	1696276.36	4708781.34
37	1697015.54	4709314.54
38	1697068.61	4709267.72
39	1697089.23	4709182.92
40	1697379.62	4709229.12
41	1697478.88	4709214.01
42	1697549.05	4709188.32
43	1697561.52	4709132.63
44	1697620.05	4709079.50
45	1697654.38	4709081.98
46	1697663.54	4709047.62
47	1697705.61	4708980.24
48	1697749.11	4709106.63
49	1697896.37	4709086.25
50	1697933.42	4709036.10
51	1697883.10	4708674.70
52	1698006.65	4708665.60
53	1698183.77	4708594.17
54	1698299.47	4708521.41

N° PUNTO	NORTE	ESTE
BASE CALCULADA	1696681.36	4710307.22

CUADRO DE AREAS PREDIO	
Construcciones	0ha + .3434 m²
Red vial, ferroviaria y terrenos asociados	2ha + .9455 m²
Mosaico de pastos con espacios naturales	469ha + .4505 m²
Bosque de galería y ripario	95ha + .4125 m²
Vegetación secundaria o en transición	10ha + .9410 m²
Lagunas, lagos y ciénagas naturales	12ha + .1492 m²
TOTAL	591ha + .2421 m²

PTO_INICIO	PTO_FIN	COLINDANTES	DIST_COLINDANTES (M)	NOMBRE_PREDIO	FOLIO_MATRICULA	CEDULA_CATASTRAL
1	5	MARLENY MOSQUERA MONTEALEGRE	1380.2	SANTA LUCIA #2	420-45242	18479000300000001008600000000
5	12	CLEOTILDE GUZMAN VILLANUEVA	2381.0	COREA N 2	NO REGISTRA	18479000300000001009900000000
12	14	MARLENY MOSQUERA MONTEALEGRE	871.1	SANTA LUCIA #2	420-45242	18479000300000001008600000000
14	17	MARLENY MOSQUERA MONTEALEGRE	1325.8	PLANADAS HOY PENJAMO	420-17230	18479000300000001017800000000
17	18	EDINSON FERNEY ORDOÑEZ CHAVEZ	375.9	LA CABAÑA	NO REGISTRA	18479000300000001028500000000
18	22	MARLENY MOSQUERA MONTEALEGRE	2072.6	LAS MERCEDES	420-41067	18479000300000001018900000000
22	23	WILSON MENESES CUELLAR	163.0	EL DIAMANTE	NO REGISTRA	18479000300000001007900000000
23	24	PEDRO ANTONIO FAJARDO RAMIREZ	654.6	EL DIAMANTE	NO REGISTRA	18479000300000001026100000000
24	25	FROILAN TRUJILLO ROJAS	337.0	BUENAVISTA	NO REGISTRA	18479000300000001009500000000
25	26	NO REGISTRA	563.9	NO REGISTRA	NO REGISTRA	18479000300000001029100000000
26	29	KARINA LOPEZ RAMIREZ	1097.1	EL MIRADOR	420-42722	18479000300000001009300000000
29	30	NO REGISTRA	259.1	NO REGISTRA	NO REGISTRA	18479000300000001029000000000
30	31	NELLY JARAMILLO ROJAS	509.8	VILLA FLOR	NO REGISTRA	18479000300000001012500000000
31	33	JOSE GABRIEL JARAMILLO ROJAS	608.7	LA VENTUROSA	NO REGISTRA	18479000300000001016700000000
33	35	ORLANDO JARAMILLO ROJAS	1124.6	LA CABANA	NO REGISTRA	18479000300000001010400000000
35	36	GUSTAVO ADOLFO TRUJILLO FIESCO	276.5	LA ESPERANZA	NO REGISTRA	18479000300000001011200000000
36	47	HILDA OSORIO TRUJILLO	1946.9	LOS CAMINITOS	NO REGISTRA	18479000300000001011300000000
47	52	ADONAY MUNOZ SANTOS	860.1	LA PALMERA	420-6090	18479000300000001016500000000
52	1	LUIS ENRIQUE CUELLAR TRUJILLO	382.8	LA PALMERA	NO REGISTRA	18479000300000001016300000000

MINISTERIO DE AGRICULTURA Y DESARROLLO RURAL

Agencia Nacional de Tierras

REPÚBLICA DE COLOMBIA

MINISTERIO DE AGRICULTURA

AGENCIA NACIONAL DE TIERRAS

DIRECCIÓN DE ORDENAMIENTO SOCIAL DE LA PROPIEDAD

SUBDIRECCIÓN DE SISTEMAS DE INFORMACIÓN DE TIERRAS

PLANO DE LEVANTAMIENTO PLANIMÉTRICO PREDIAL

PLANO No. AAAAA 00000 00

MAPA DE UBICACIÓN GENERAL

Escala

175 87.5 0 175 350 525 700 Meters

1 centímetro en el plano es igual a 20 metros en terreno

PTO_BASE

Lindero_Predio

DIRECCION_SOLICITA

Dirección de Acceso a Tierras

DIST_COLINDANTE

Cobertura_Lev_Top

DESCRIPCION

Bosque de galería y ripario

Lagunas, lagos y ciénagas naturales

Mosaico de pastos con espacios naturales

Red vial, ferroviaria y terrenos asociados

Vegetación secundaria o en transición

Zonas industriales o comerciales

Linea_Colindancia

CAMBIO_COLINDANCIA

PTO_DETALLE

DIRECCIÓN DE ACCESO A TIERRAS

COMPRA DIRECTA

CONVENIO FONDO DE REPARACION A VICTIMAS

PREDIO "VILLA VAZQYEZ"

CÉDULA CATASTRAL : 18479000300000001010000000000

MATRÍCULA INMOBILIARIA : 420-70314

DEPARTAMENTO : 18-CAQUETA	MUNICIPIO : 479-MORELIA	VEREDA : LA CANDIDO
PROPIETARIO : FONDO DE REPARACION A VICTIMAS		AREA LEVANTAMIENTO : 591 Ha + 2420 m2
REALIZO : Henry Alejandro Moreno M. M.P.01-17300 CNPT	REVISÓ : Dirección General	FECHA : ABRIL DE 2025
		ARCHIVO : VILLA VASQUEZ
PARAMETROS GEOGRAFICOS: Magna-Sirgas / Origen - Nacional Proyección : Transversa de Mercator Elipsoide: GRS80 Latitud: 4° N Longitud: 73° W Falso Norte: 2.000.000 Falso Este: 5.000.000 Factor de Escala: 0.9992	CARTOGRAFÍA BASE : PLANCHA 1:25.000 - 432IIA	TIPO LEVANTAMIENTO : GPS GNSS DIFERENCIAL GPS CHCNav PRESICION MODELO CHC I80

NOTA:
Los linderos del predio fueron reconocidos en compañía del mayordomo.