


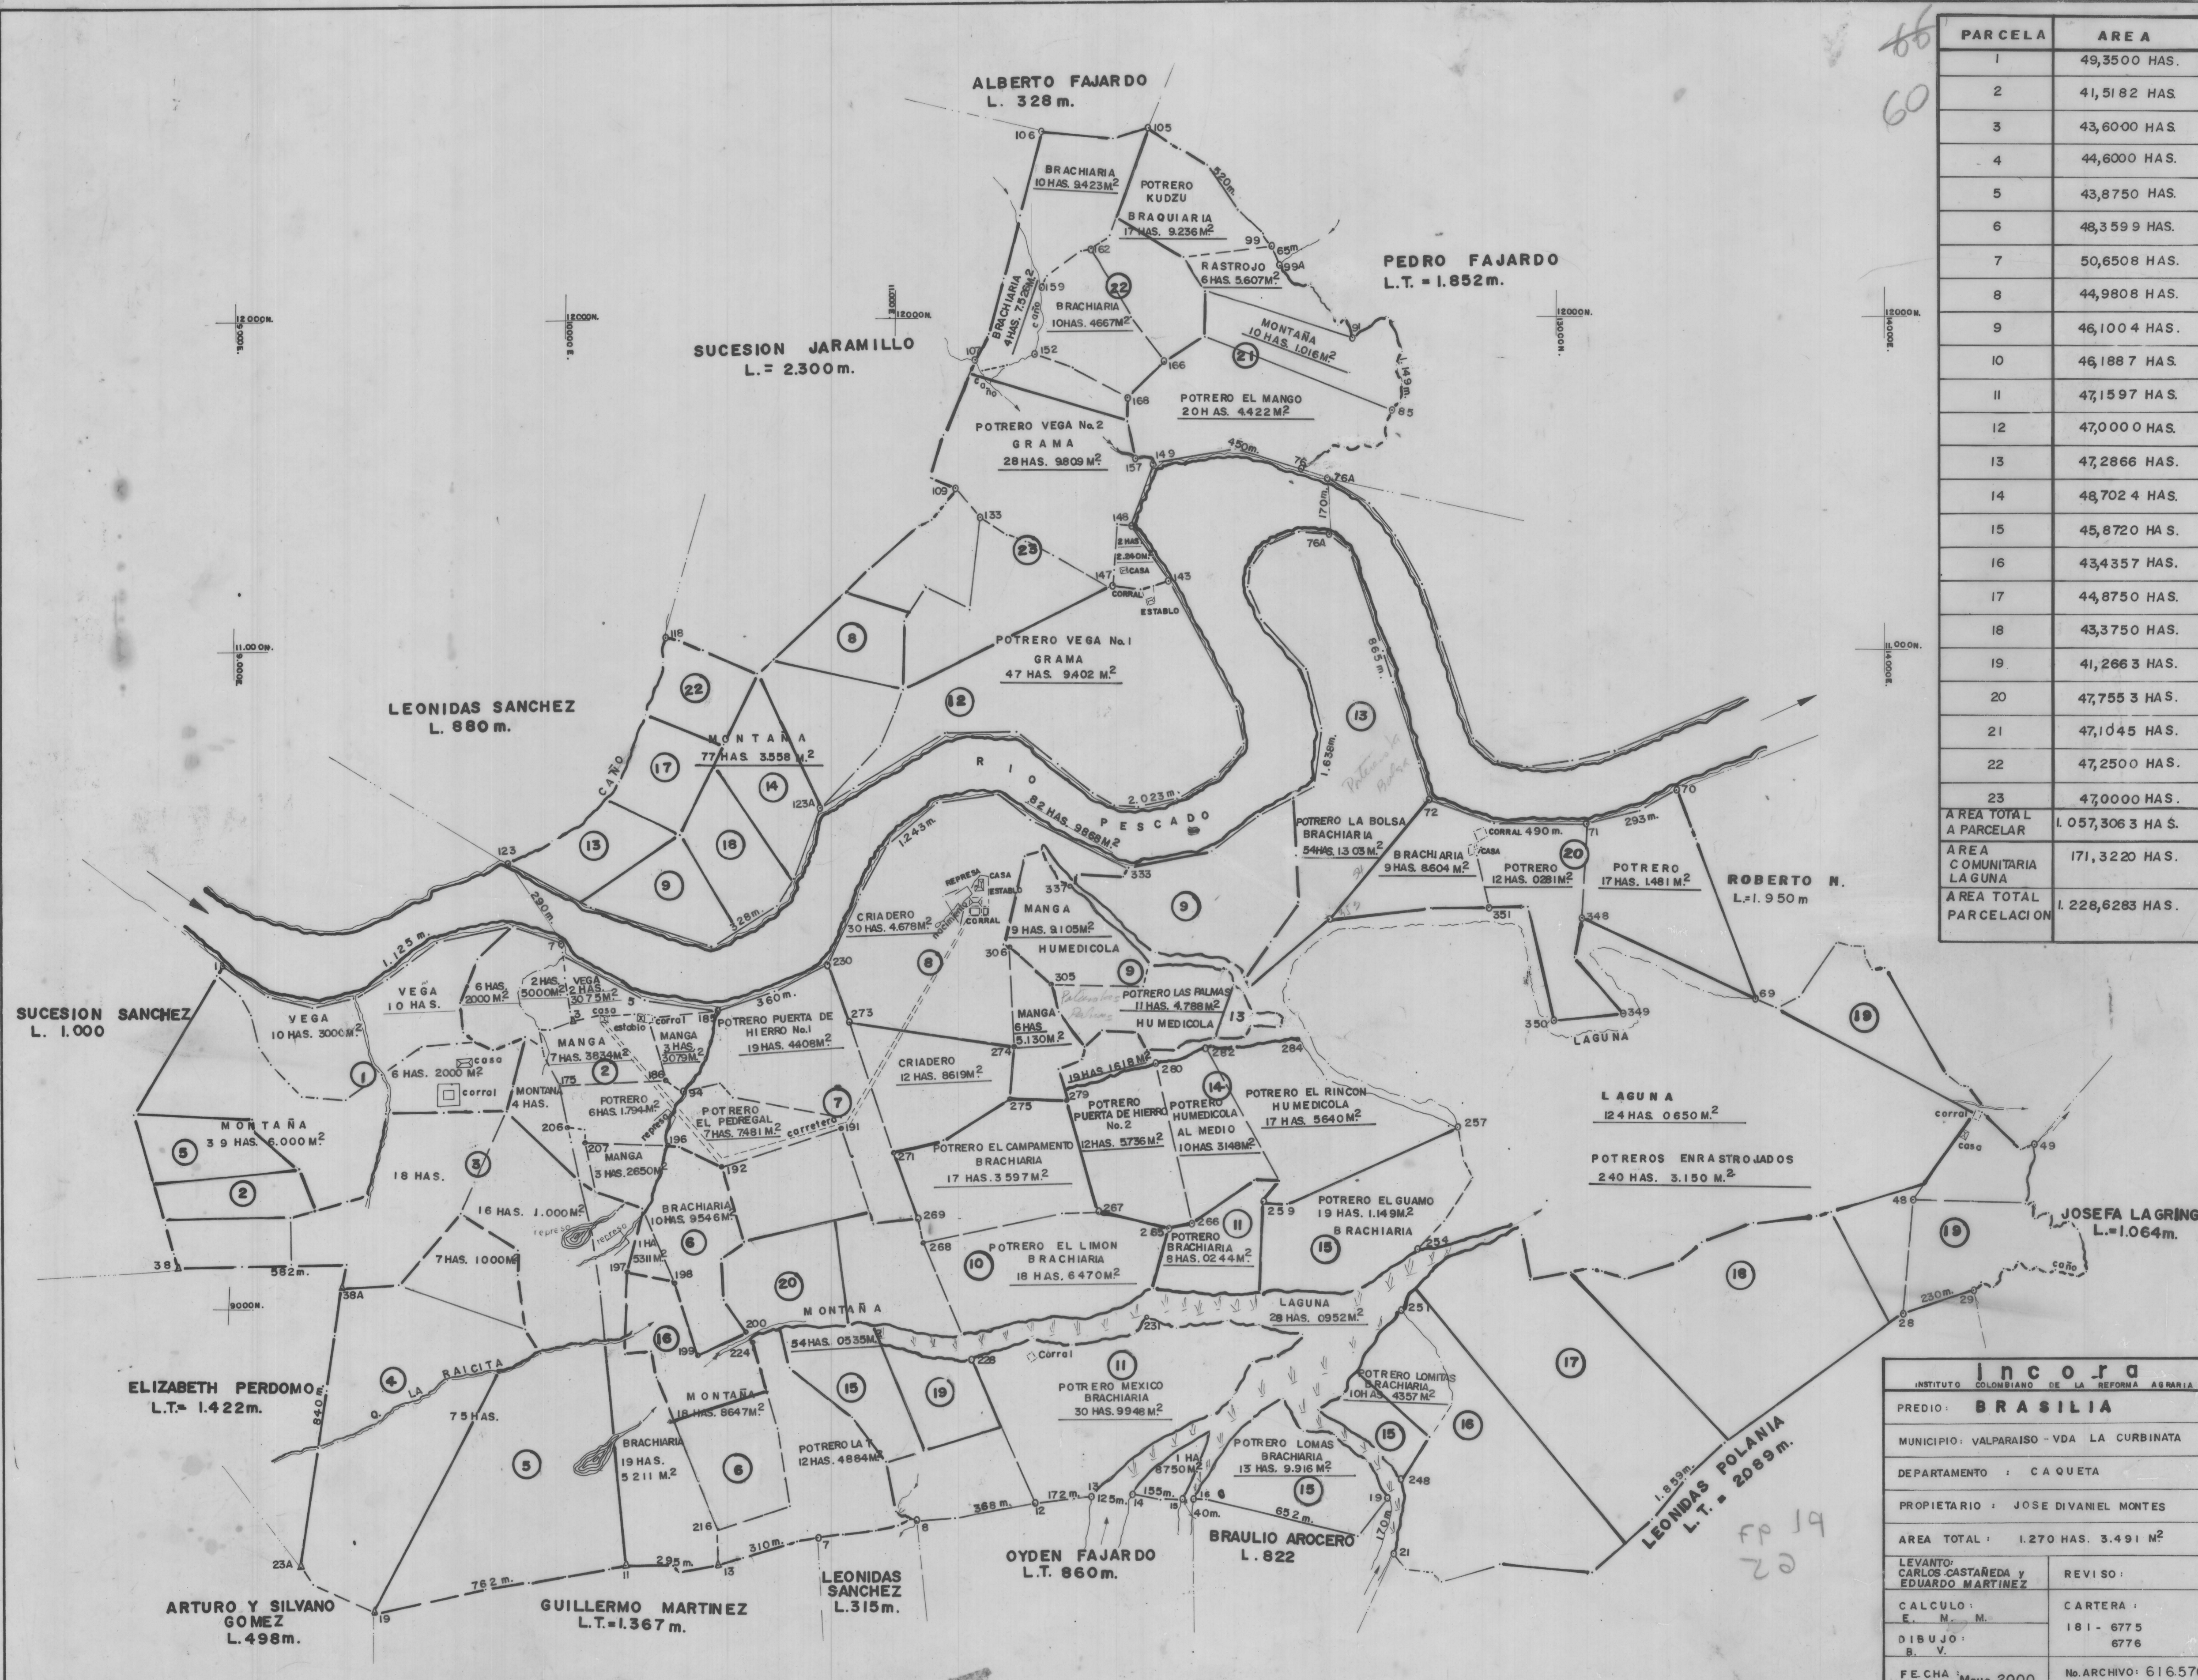

PARCELA	AREA
1	49,3500 HAS.
2	41,5182 HAS.
3	43,6000 HAS.
4	44,6000 HAS.
5	43,8750 HAS.
6	48,3599 HAS.
7	50,6508 HAS.
8	44,9808 HAS.
9	46,1004 HAS.
10	46,1887 HAS.
11	47,1597 HAS.
12	47,0000 HAS.
13	47,2866 HAS.
14	48,7024 HAS.
15	45,8720 HAS.
16	43,4357 HAS.
17	44,8750 HAS.
18	43,3750 HAS.
19	41,2663 HAS.
20	47,7553 HAS.
21	47,1045 HAS.
22	47,2500 HAS.
23	47,0000 HAS.
AREA TOTAL A PARCELAR	1.057,3063 HA S.
AREA COMUNITARIA LAGUNA	171,3220 HAS.
AREA TOTAL PARCELACION	1.228,6283 HAS.

INCORA	
INSTITUTO COLOMBIANO DE LA REFORMA AGRARIA	
PRECIO: BRASILIA	
MUNICIPIO: VALPARAISO - VDA LA CURBINATA	
DEPARTAMENTO: CAQUETA	
PROPIETARIO: JOSE DIVANIEL MONTES	
AREA TOTAL: 1.270 HAS. 3.491 M²	
LEVANTO: CARLOS CASTAÑEDA y EDUARDO MARTINEZ	REVISO:
CALCULO: E. M. M.	CARTERA: 181 - 6775
DIBUJO: B. V.	6776
FECHA: Mayo 2000	No. ARCHIVO: 616.570